

不是冻结一张总图，而是冻结三道可复算的选择门

日常公共带保持公共目标不变；官方边界、批准容量与影响闭环决定空间组织。

主线

以日常公共带串联遗址、社区、研学与便民服务；以受益 / 成本 / 责任证据决定保全、织补或避让。

连续骨架保全案

成立门

官方边界完整包含公共带与节点；六处东西联络全部通过红线、权属和工程核查。

淘汰门

任一处联络未通过，立即淘汰“全连续”主张，转入织补或避让。

当前只允许

核查、标线、可移家具与运营测试；实体连续工程不得先行。

存量界面织补案

成立门

$\Delta GFA \leq 0$ 且 $S \geq 0$ ；经核合法保留的可用首层足以承接公共服务节点。

淘汰门

$S < 0$ ；或 $\Delta GFA > 0$ 且 $R_{\text{新增}} > R_{\text{存量}}$ 。

当前只允许

存量盘点；消防、权属、结构与开放协议签认后再试点。

邻里避让回路案

成立门

受影响户数 ≥ 1 ，且缓解预算仍为 unknown、资金未生效或行动未验收。

淘汰门

所有拟建界面影响户数均为 0；或每项非零影响均有审核行动、资金与验收责任。

当前只允许

仅 R1：可撤导视、活动与时段规则；不开挖、不拆建、不做永久阻隔。

对方案不利的自评

0/6

横向联络获得正式红线、权属与工程可行性确认

图形连通不等于真实连通。连续骨架是最先可能被淘汰的一案。

代价侧：保持 unknown

affected_household_count

需授权且去重的住户 / 房屋资料与专业影响范围

mitigation_budget_cny

需审核工程量、单价版本、资金承诺与审批状态

duty_closure_ratio

需生效触发器、到期条件、行动状态与验收记录

先行判断

可以先做

基线调查 · 无障碍核查 · 运行规则 · R1 可逆小修

必须停


关键资料 unknown 时，不启动 R3 永久工程。

九类提交几何：一条日常公共带，三种证据等级

总体图表达概念索引，不替代官方红线、现状调查、道路红线或工程线位。

提交图层总平面

所有图层叠合，坐标轴与比例尺不作为正式判断

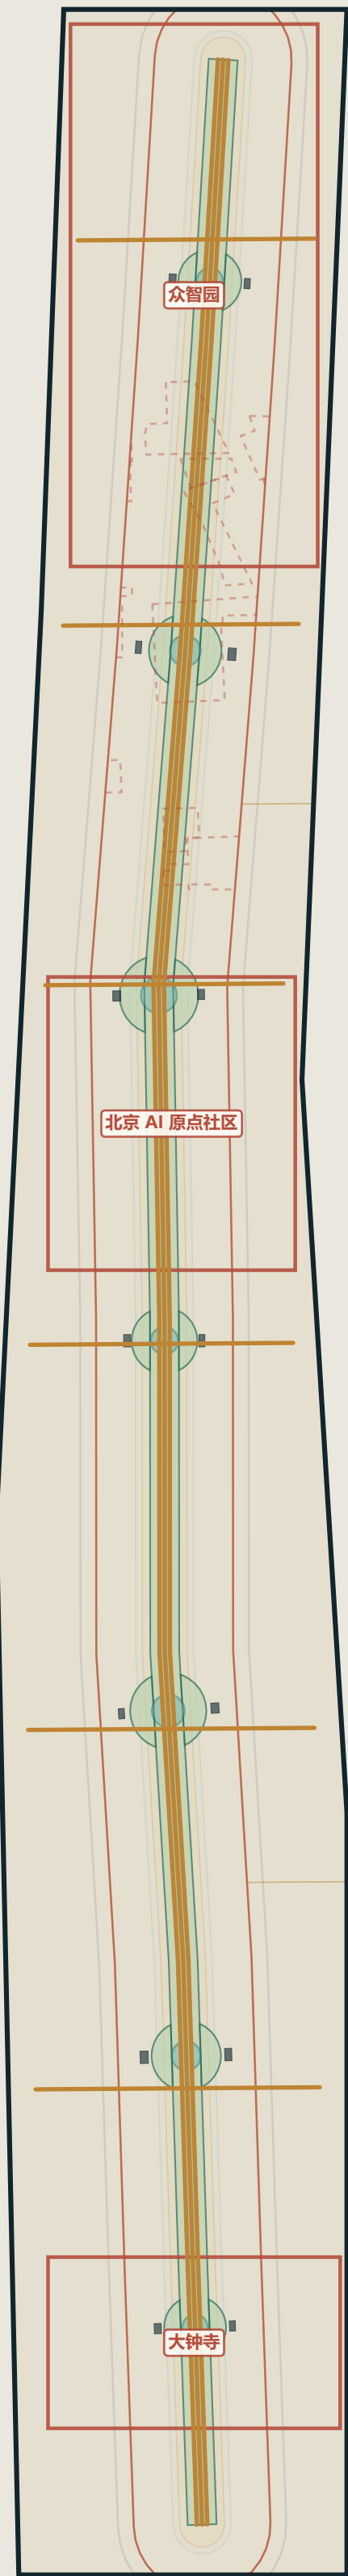

- 总体设计范围: provisional
- 概念用地 / 慢行
- 公共空间
- 分期
- 重点区域: provisional
- 绿地
- 概念建筑基底
- 约束 / 待核线索

三层范围关系

统筹研究范围 43.61 km²

总体设计范围 11.41 km²

重点区域: 官方预告名义面积

众智园 1,921,000 m² · AI 原点社区 1,043,000 m² · 大神寺 720,000 m²

三处粗略多边形仅定位，不得以几何复算值替代名义面积。

公共带结构复算

8 公共空间要素: 连续公共带 + 七个节点

9 道路要素: 三条南北线 + 六条东西联络

1 个图形连通分量 / 0 个图形断点

工程核验断点、服务半径与容量仍为 unknown。

比率纪律

green_ratio 0.106694

public_space_ratio 0.033175

分母一律为总体设计范围 11.41 km²; 43.61 km² 只作语境。


界面设计不是尺寸表：先核受益对象，再锁代价与责任

典型段落复用已定稿图；右侧建立同一干预单元的受益 / 成本 / 责任与 R1-R3 回退路径。

典型段落 A-A'：京张铁路遗址公园与既有居住界面


典型段落 A-A'：京张铁路遗址公园与既有居住界面

平面与界面策略示意·代价与责任的空间落点

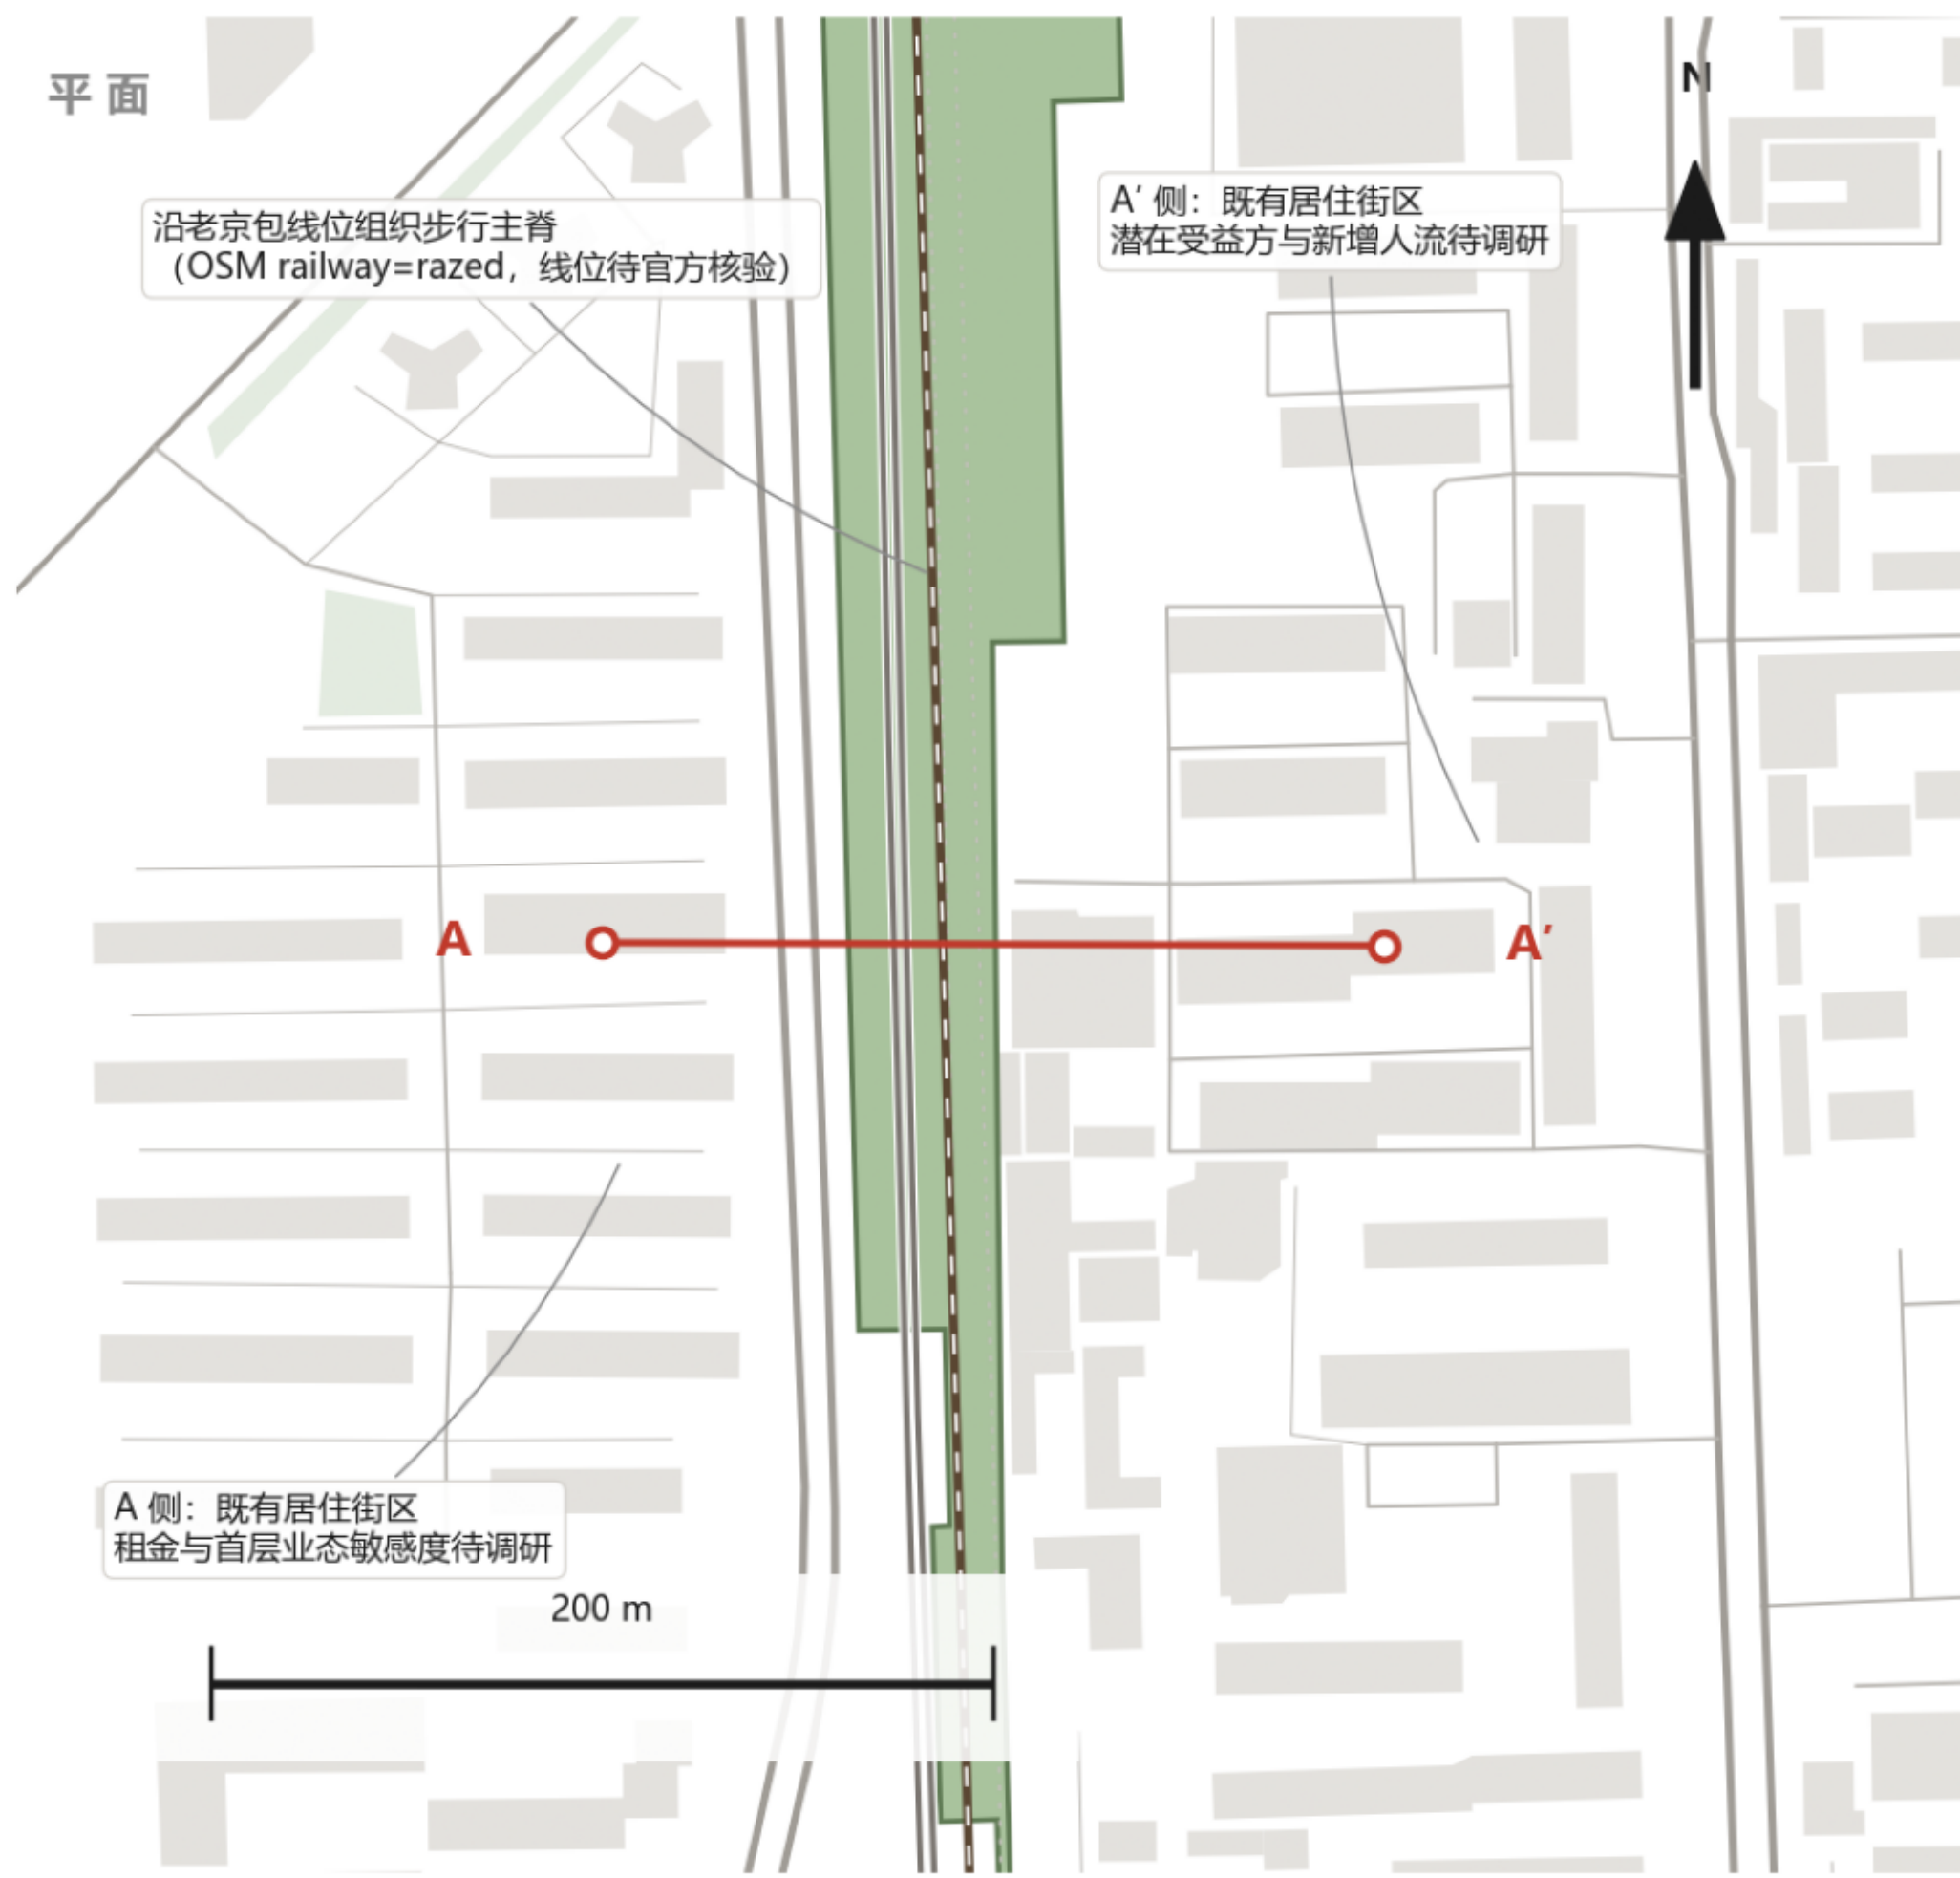

图例：既有建筑、绿地、遗址公园、截线位置 A-A'、老京包线位 (OSM razed, 待核)、地上高架线、地下线路投影 (非地面轨迹)。
底图：© OpenStreetMap contributors (ODbL 1.0)。OSM 仅作参考，不生成任何正式尺寸；边界、面积、道路红线、建筑用途与层数、剖面尺度均待官方资料或现场测绘确认。右侧为界面策略示意，非现状剖面测量，不作施工依据。

界面策略示意 A-A' (非现状测量；尺度、层数、业态均待核)

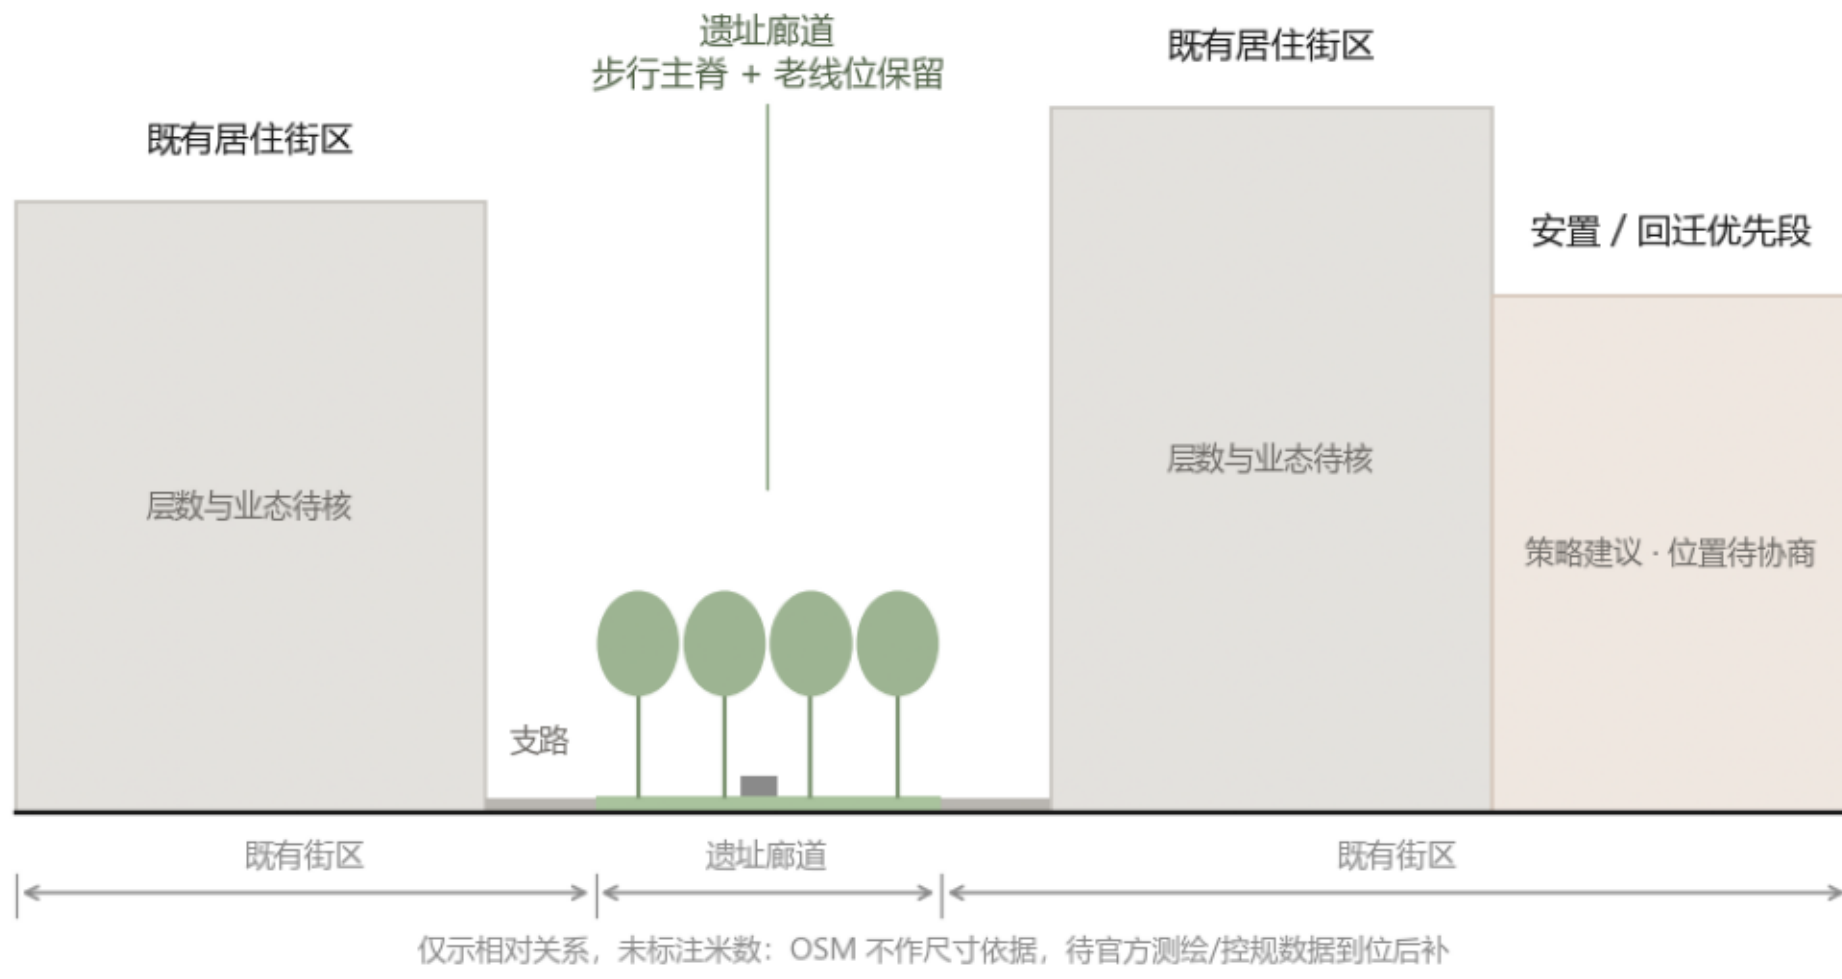

谁受益·谁付代价·谁负责 (本段)

- 受益**：区域可达性提升；新增就业与机构受益方待调研核实
- 代价**：沿廊道既有住宅：施工期噪声、租金上行、首层小微业态被替换 (待调研)
- 责任**：建议责任主体 (待协商)：过渡商铺位、回迁优先、租金缓冲期、噪声阈值与申诉入口

受益 / 成本 / 责任落点

受益

公共通行、日常停留、服务可达与资源共享；宣传曝光和预测客流不进入受益总量。

成本

施工、绕行、噪声、经营、维护、能源、隐私与空间排他；影响对象与金额均保持 unknown。

责任

触发条件、提出人、出资人、复核人、截止条件、验收证据与状态必须绑定同一 intervention_id。

受益不能抵消某一对象尚未缓解的损失。

回退成本分级

R1 可撤销

标线、导视、可移家具、活动时段、软件与传感设备

可先测试；回退含表面恢复、数据退役与通知使用者

R2 可修复

铺装、种植、雨水小设施、室内隔断与机电适配

需补基层、植物、设备和营业状态的恢复路径

R3 难逆 / 不可逆

拆除、新建永久结构、地下管线、桥隧、长期权利变更与搬迁

关键资料 unknown 时不得启动；金额继续为 unknown